

Brandon Avalos

Hume Vertical Studio
SCI-Arc FA26
Midterm Review, October 19, 2026

ARROYO SECO STABLES, SOUTH PASADENA




“After the revolution, who’s going to pick up the garbage on Monday morning?”


MIERLE LADERMAN UKELES, MANIFESTO FOR MAINTENANCE ART, 1969

PLACE:
ARROYO SECO
AERIAL STRIP,
CUT ALONG
CHANNEL EDGE

SITE PLAN / NORTH UP

Arroyo Seco Stables, South Pasadena. Lower Arroyo, downstream of Devil’s Gate Dam.

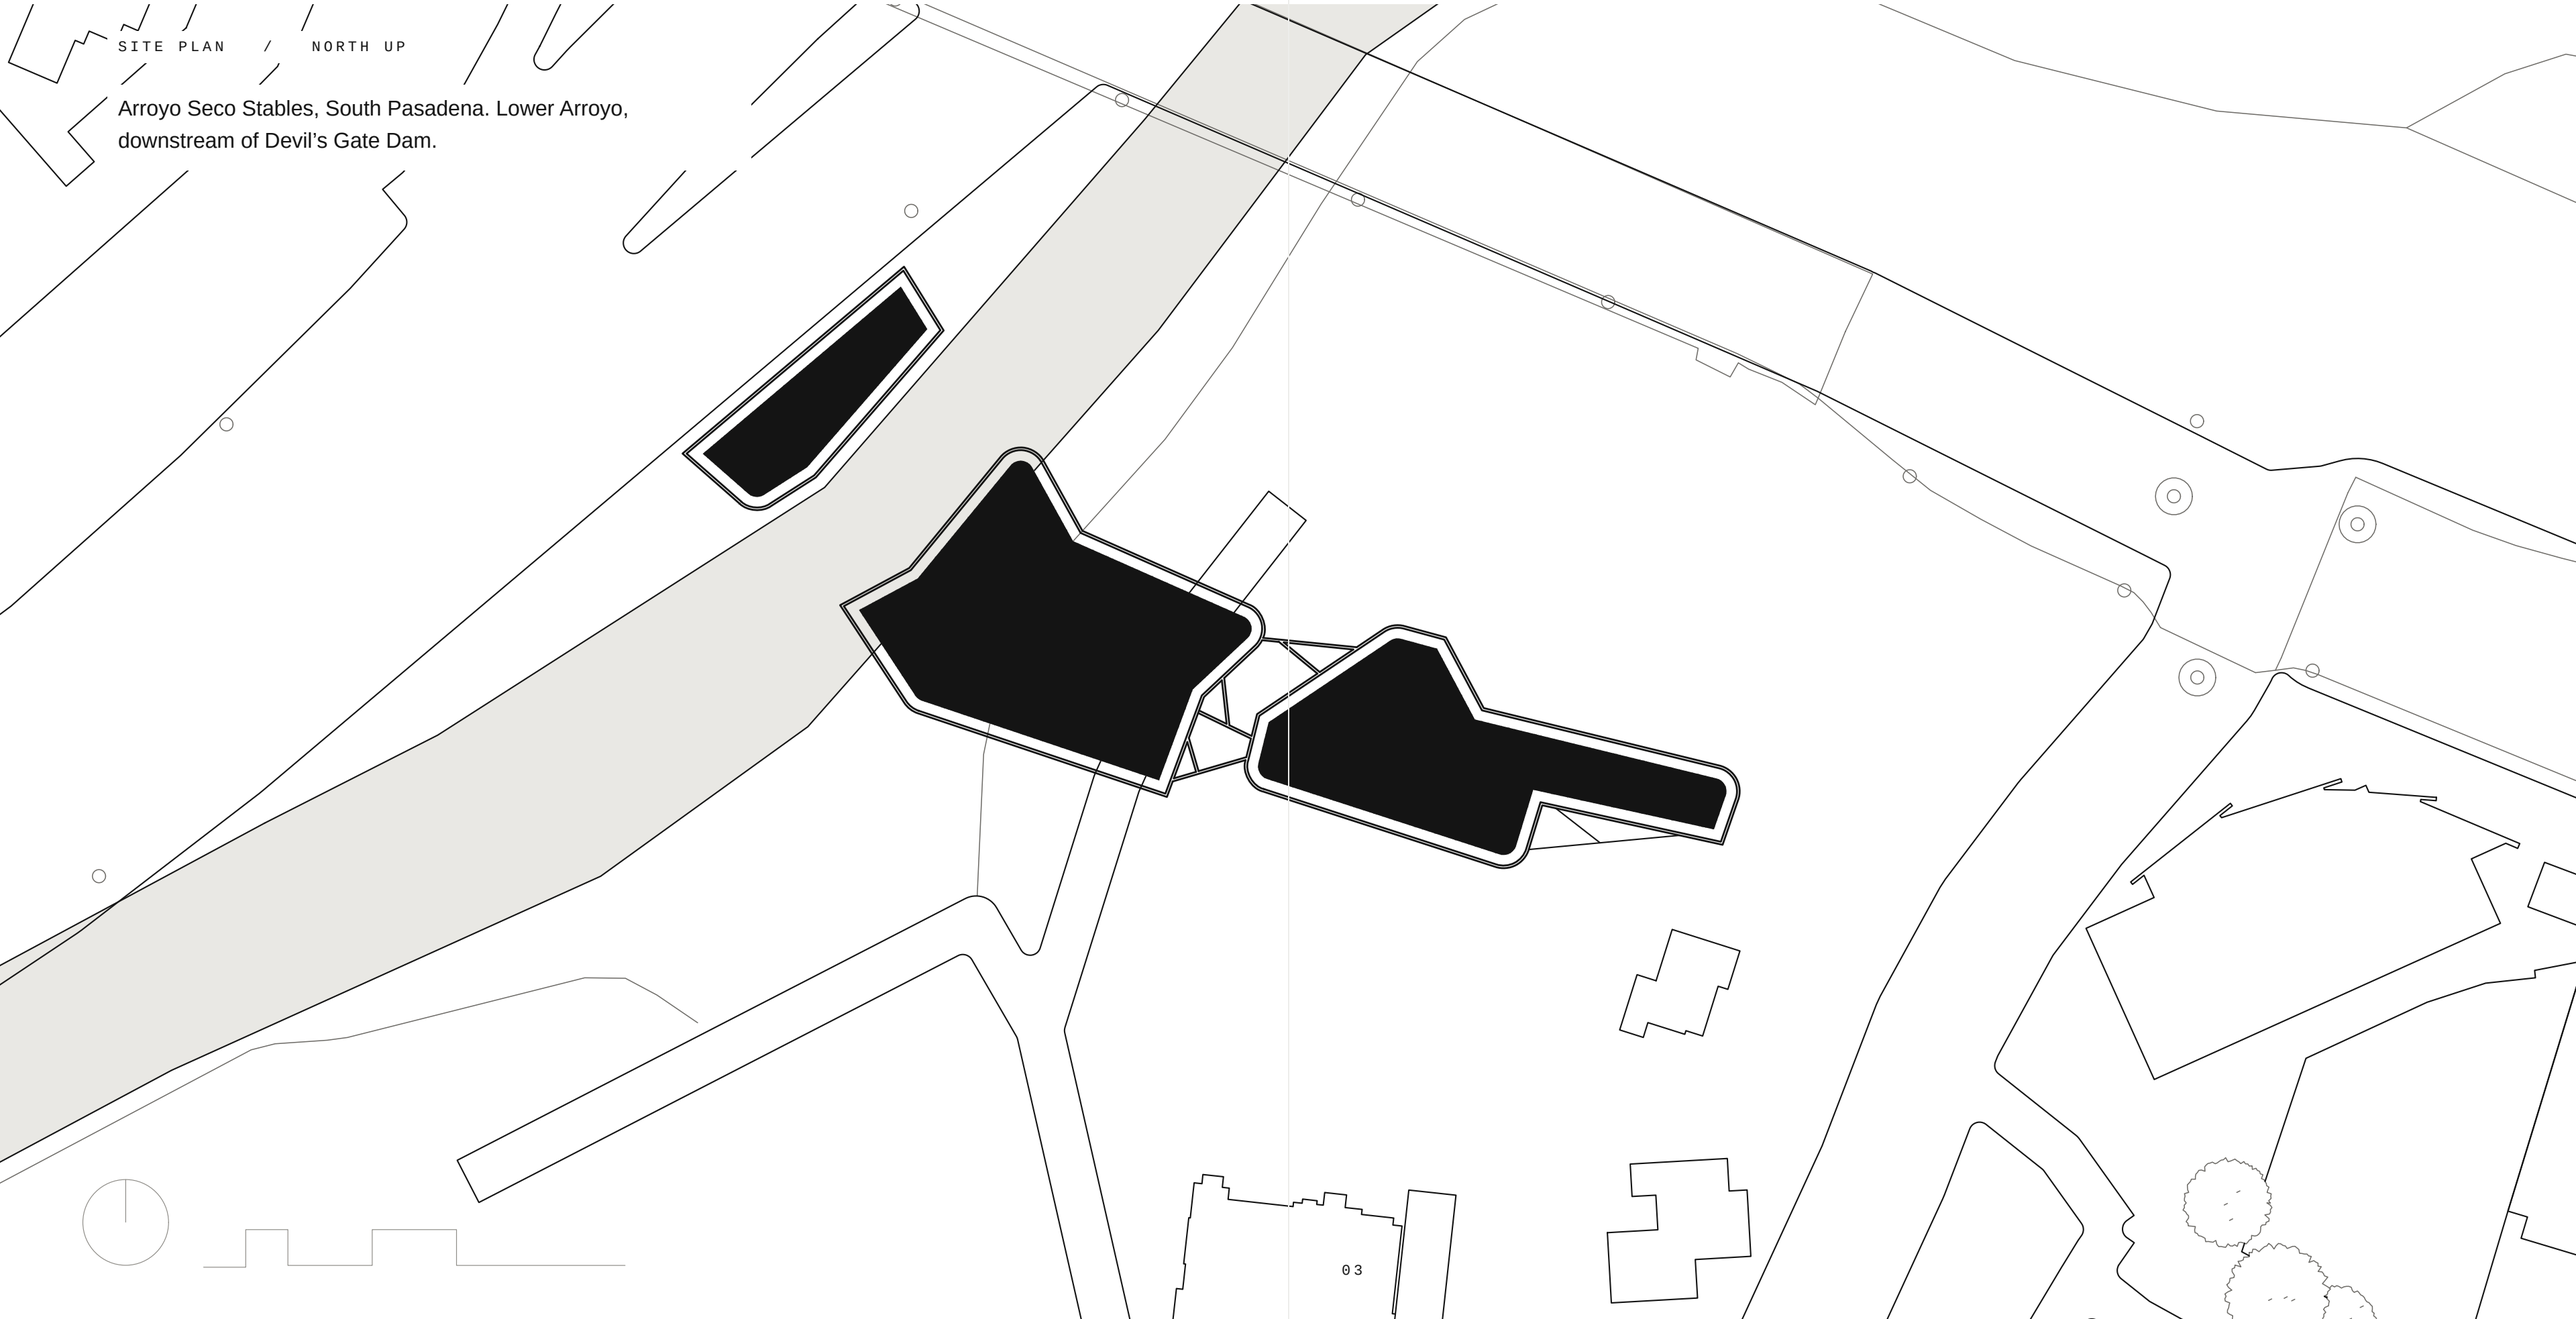

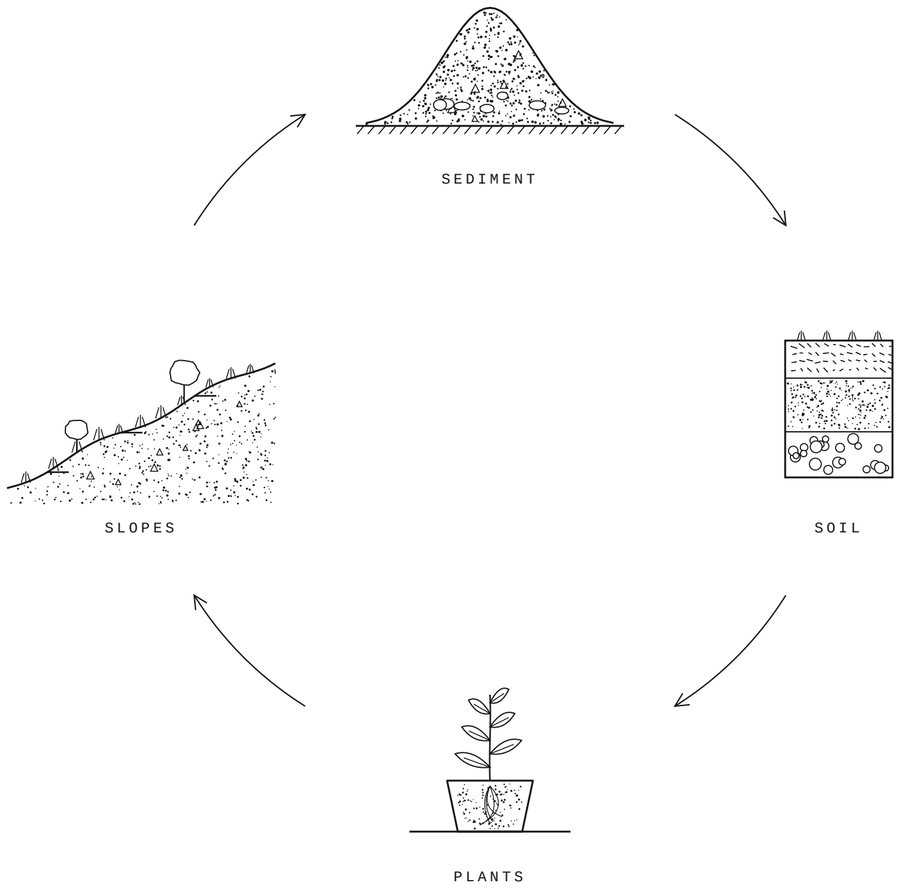

Maintenance that is hidden gets abandoned. A sediment node makes it public, permanent, and productive.

PROBLEM

Fire-loosened sediment from the San Gabriels is trapped at Devil's Gate Dam, removed each year, and trucked away as waste out of public view.

PROPOSAL

A public station where the river's maintenance becomes visible, paid work, and that work rebuilds the land, the river, and the people who do it.

SEDIMENT > SOIL > PLANTS > SLOPES > LESS SEDIMENT



JOINT / 06-07

1" = 1'-0"



SLIVER / 08-09

1/4" = 1'-0"




BUILDING / 10

1/4" = 1'-0"



SITE / 11-12

1/32" = 1'-0"

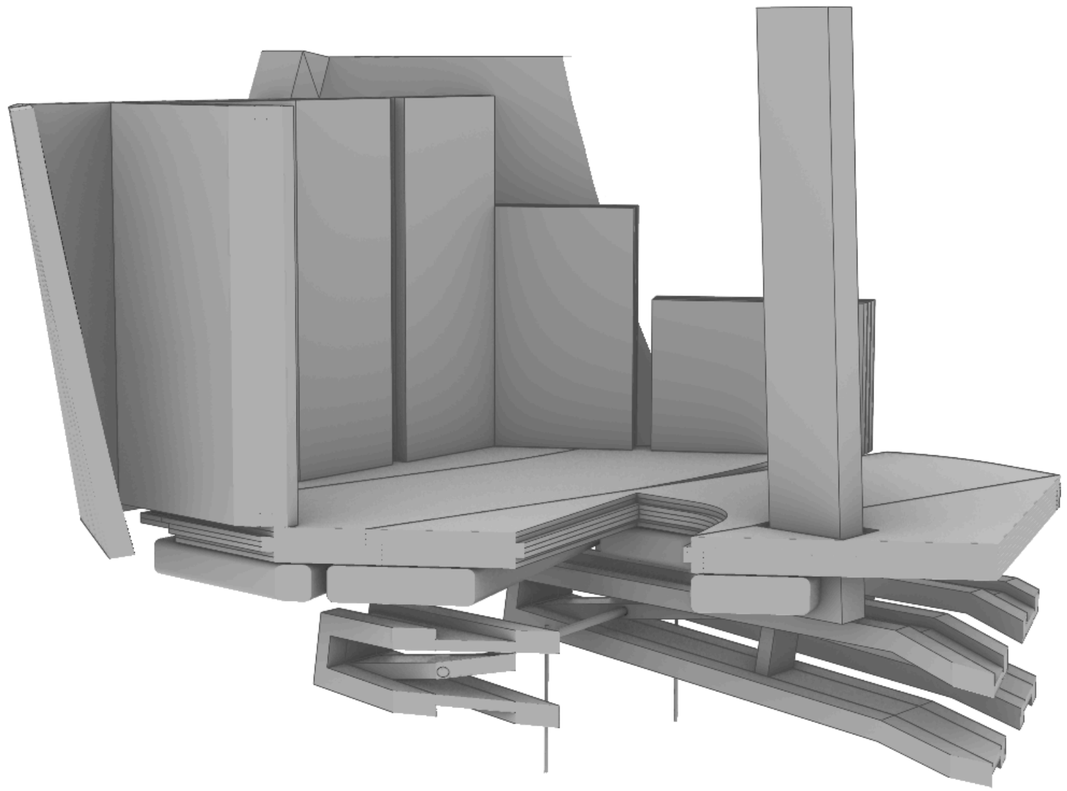


DETAIL DRAWING

1" = 1'-0"

[One sentence on what this drawing proves.]

FLOOR PLATE / TOP TO BOTTOM

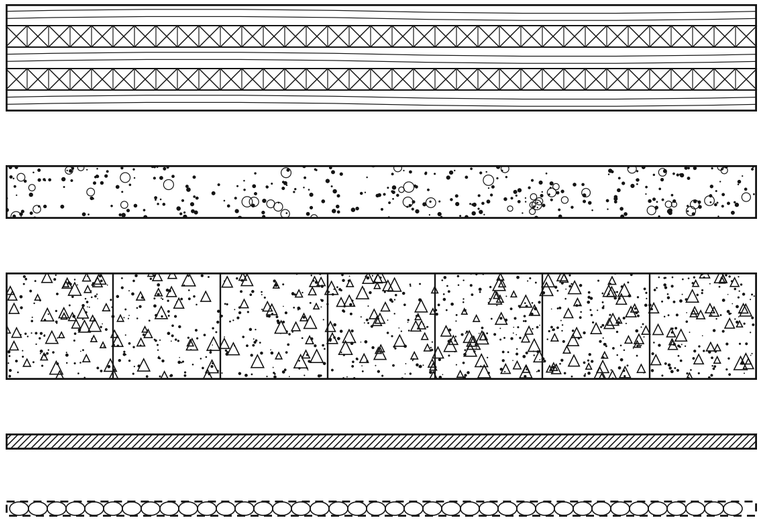

CLT
STRUCTURE

CORK
IMPACT, THERMAL


SEDIMENT EARTH TILES
MASS, CEILING BELOW

DYNEEMA BINDING
RETENSIONED BY CREW

STEEL STOP CHAIN
HIDDEN FAIL-SAFE

The floor is made of what the node processes. The Dyneema creeps, the earth layer sags, and the crew retensions it: maintenance performed in public view.

WALL / OUTSIDE TO INSIDE

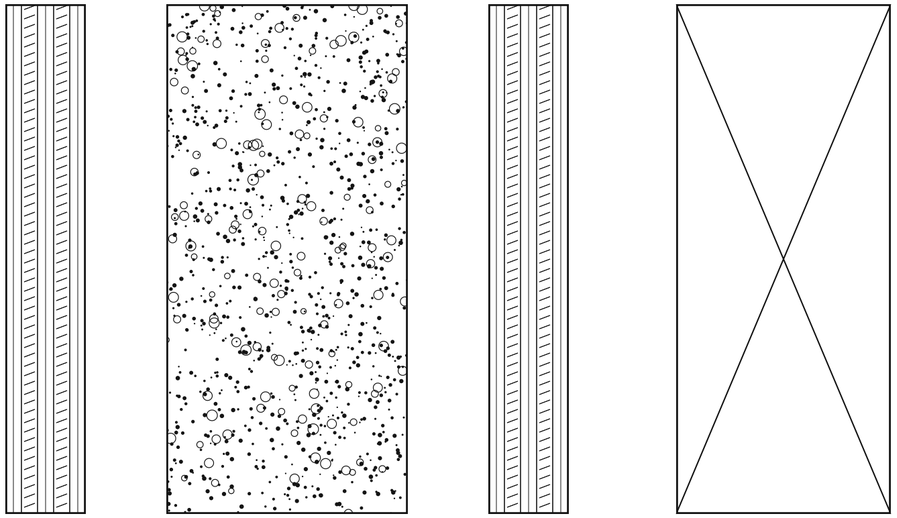

SKIN
CLT OR PLY


CORK CORE
INSULATION, DAMPING

SKIN
CLT OR PLY

SPACER FRAME
EDGES, OPENINGS

Two thin skins held apart act like an I-beam: stiffness from depth, not mass. The cork core gives continuous insulation and acoustic damping.

EXPLODED IN SECTION / HATCHED BY MATERIAL

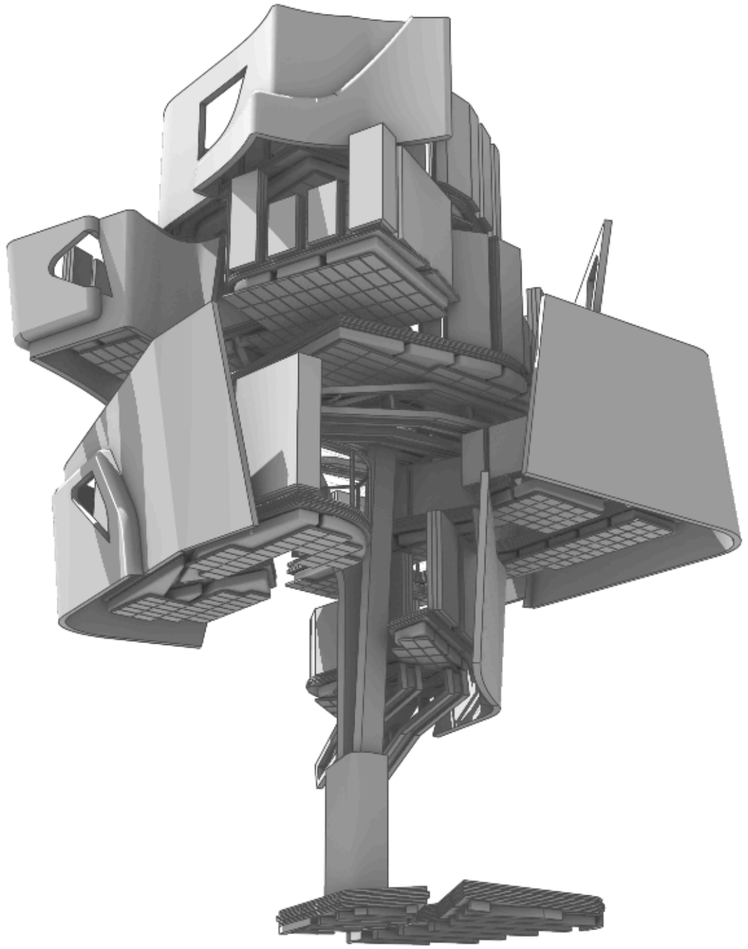


SLIVER / MODEL RENDER

SLIVER DRAWING

NOT TO SCALE

[One sentence on what this drawing proves.]

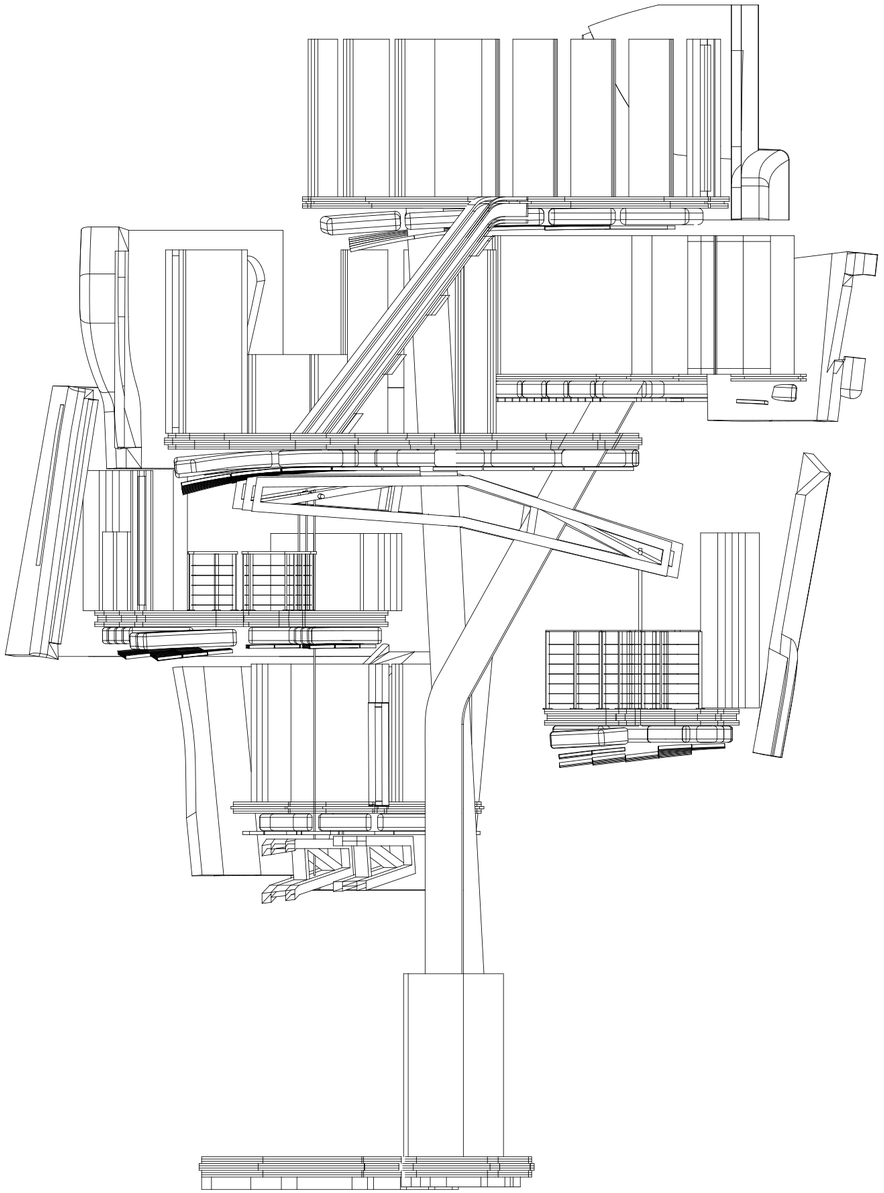

34° 06' 43.8" N 118° 10' 37.1" W

PLACE: SLIVER SECTION MODEL
FULL BLEED

SLIVER SECTION MODEL

1/4" = 1'-0"

PLACE: MODEL DETAIL

[One sentence on what this drawing proves.]

BUILDING SECTION


1/4" = 1'-0"




[One sentence on what this drawing proves.]

OVERALL SECTION / SITE CONDITION

1/32" = 1'-0"

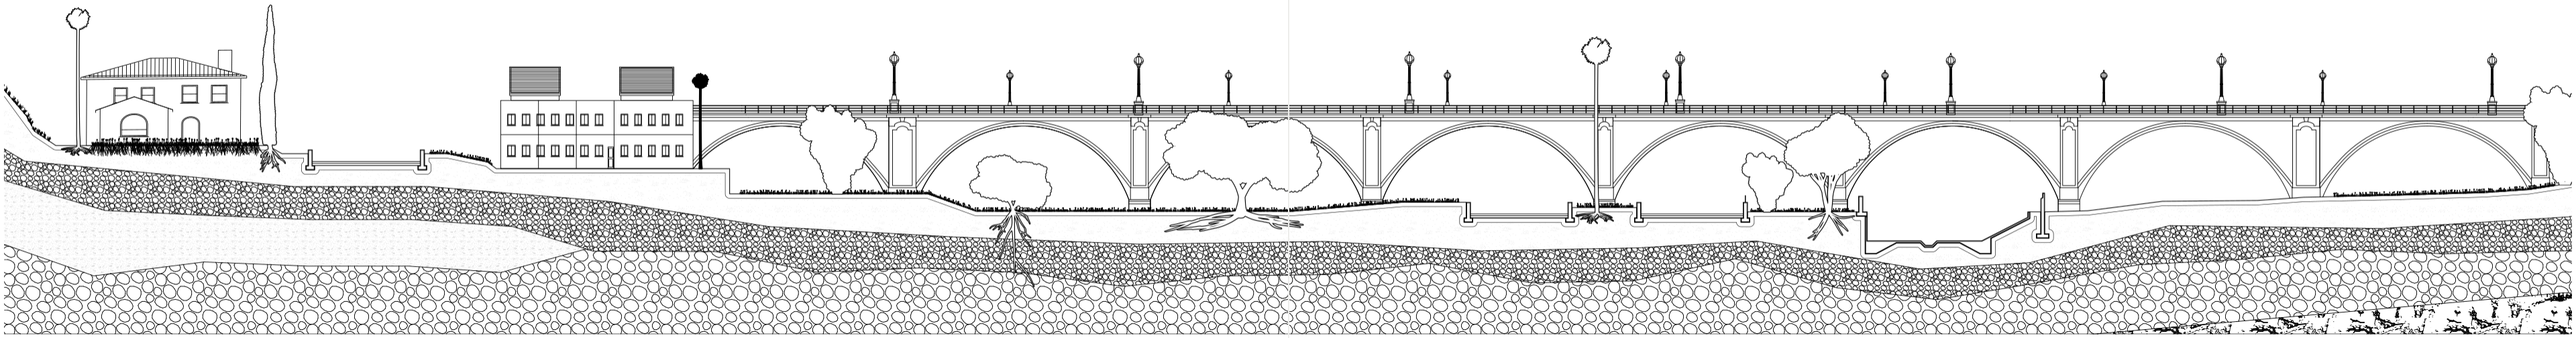

[One sentence on the site condition this section reveals.]

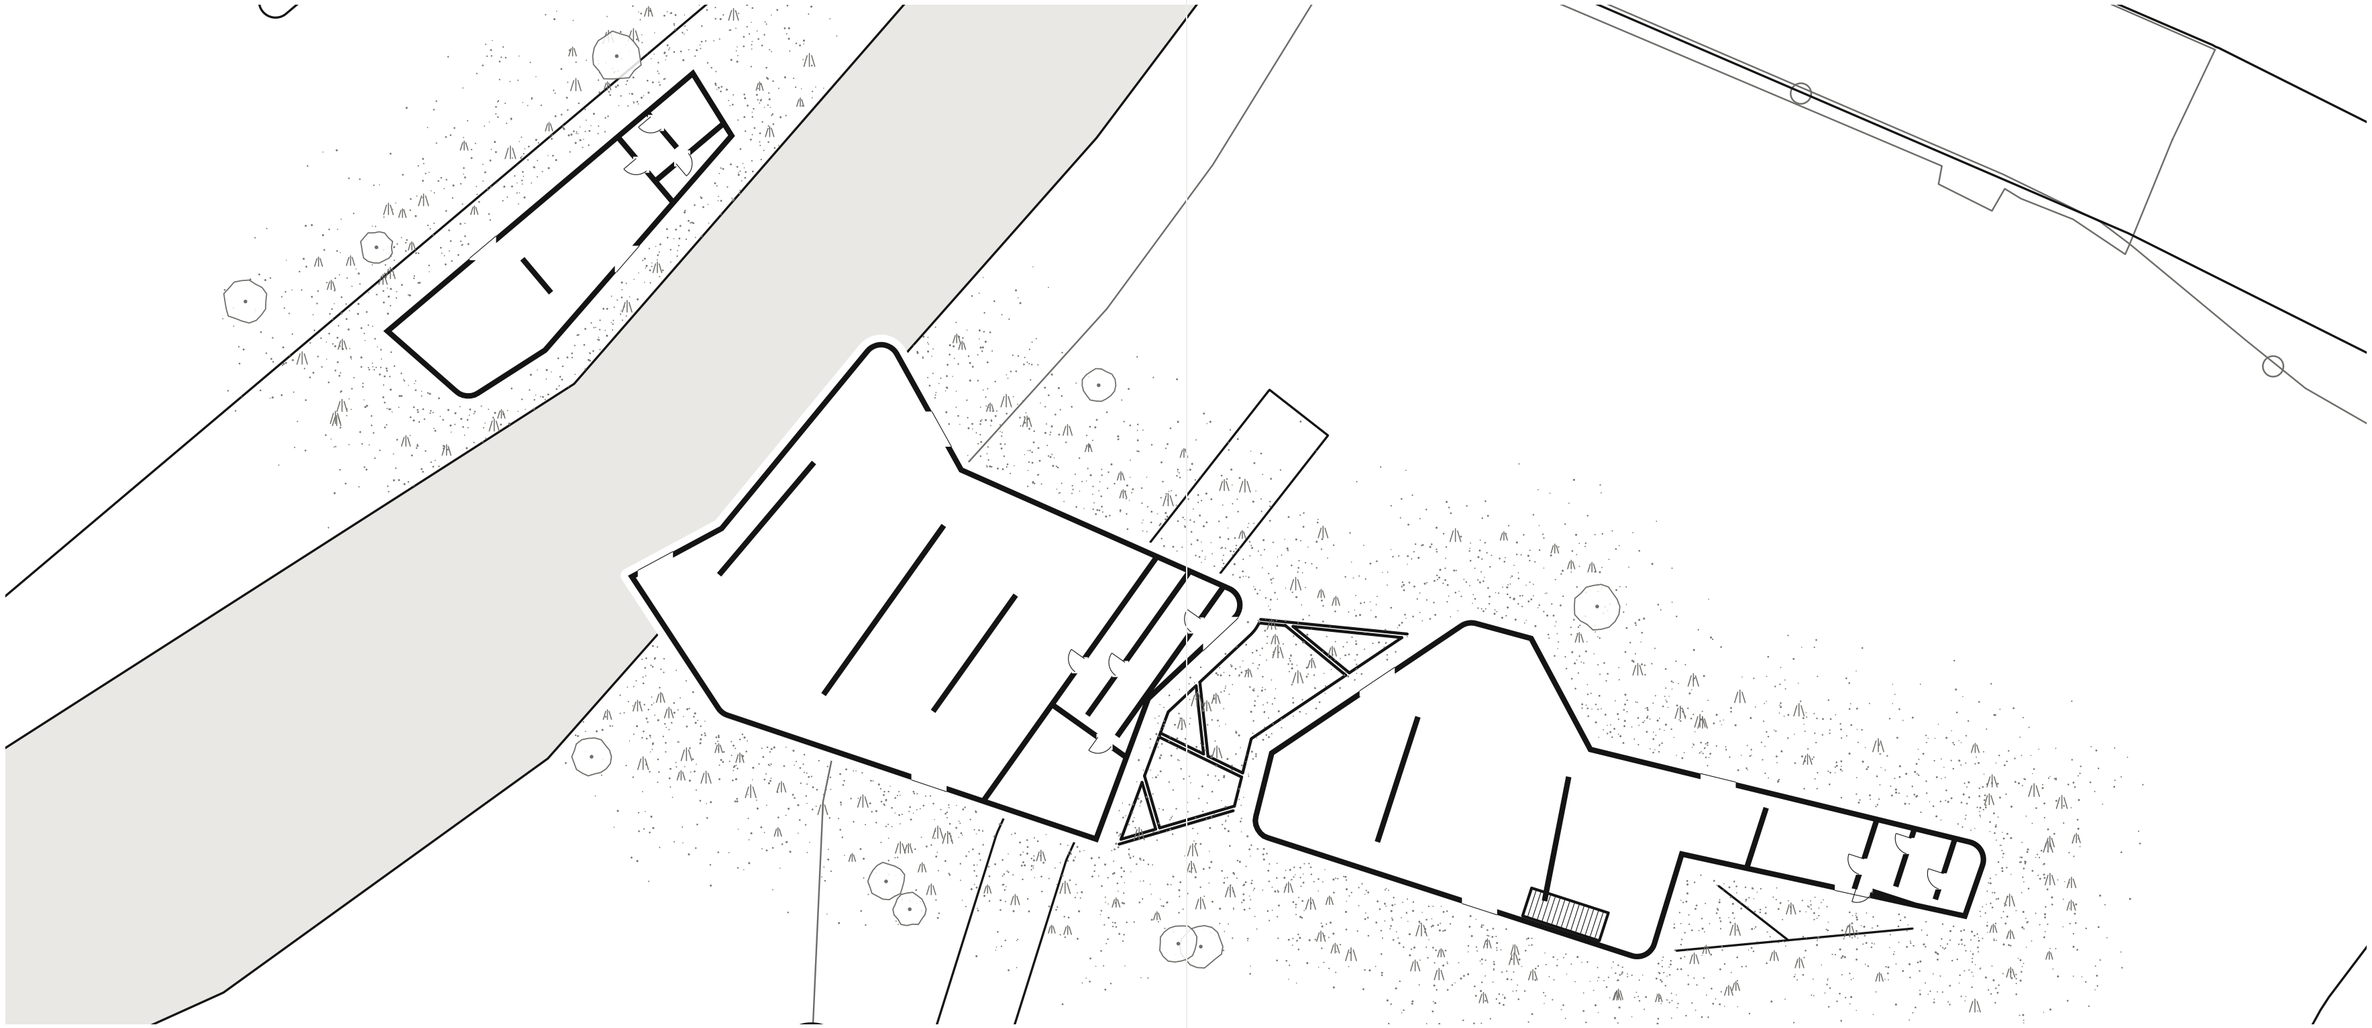

34° 06' 43.8" N 118° 10' 37.1" W

PLACE: MODEL PHOTOGRAPH 01
FULL BLEED

PLACE: 03

PLACE: MODEL PHOTOGRAPH 02